AMBIENTE 1

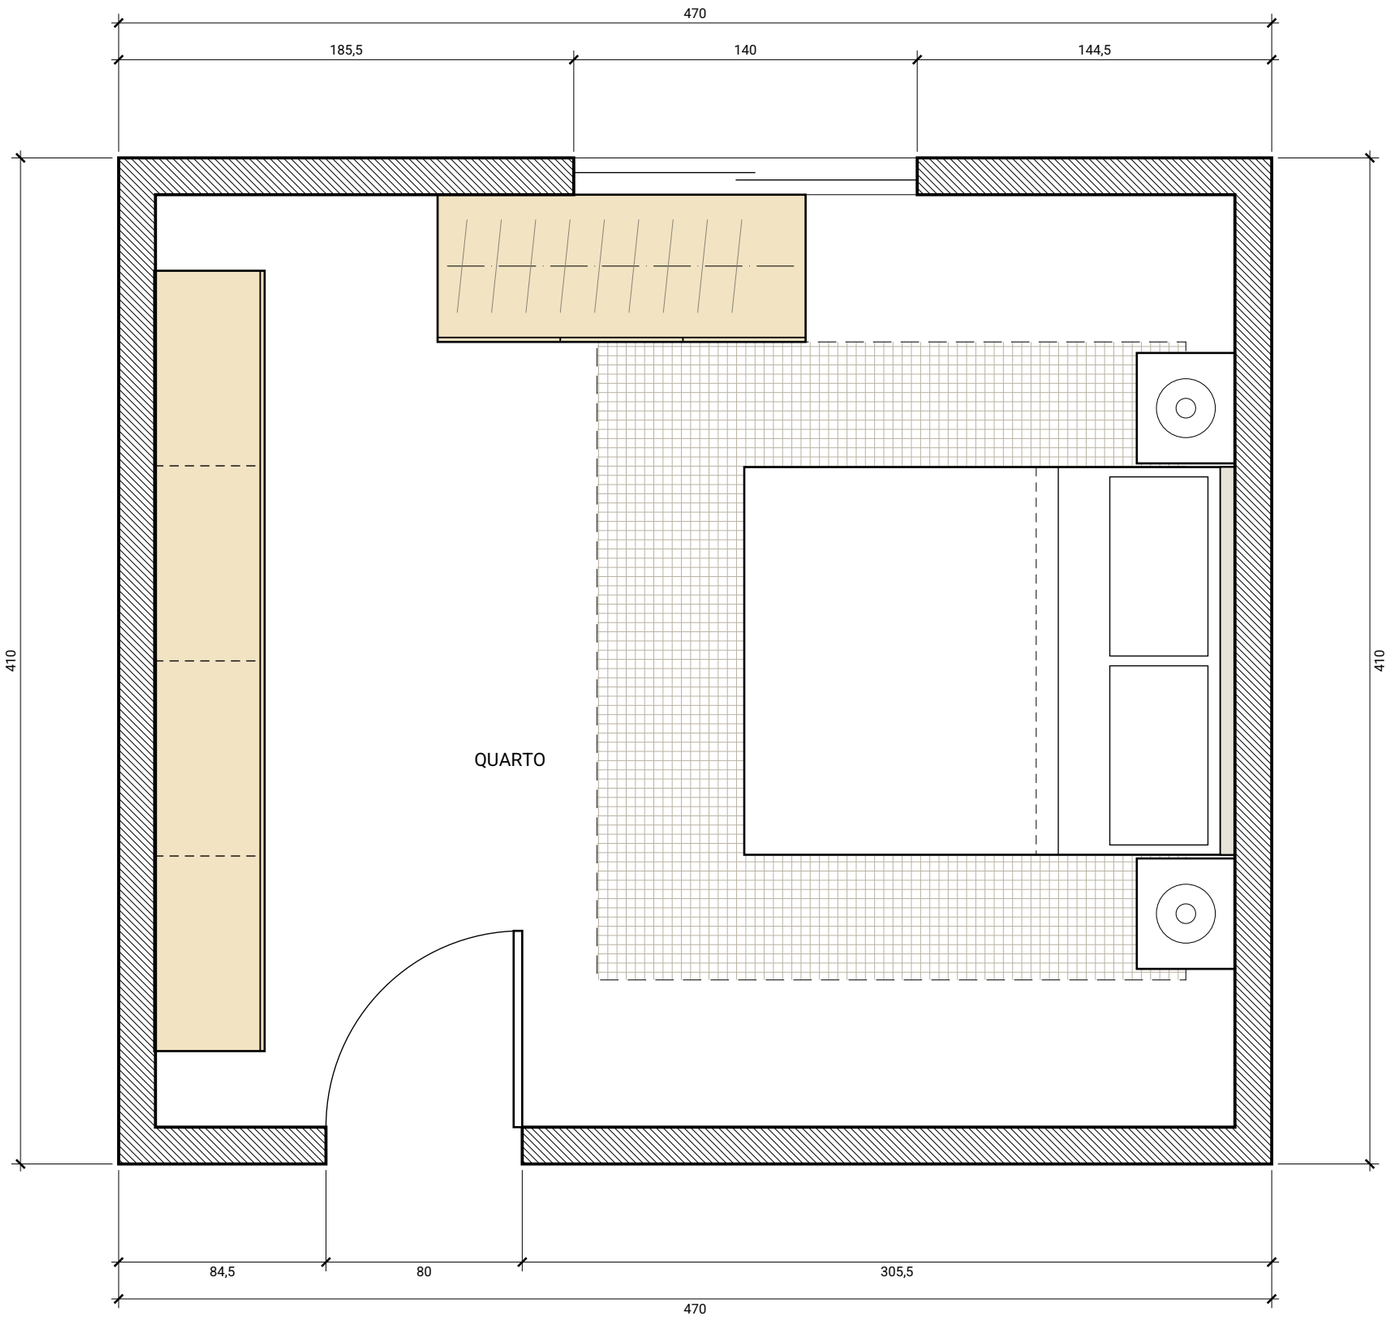

ESCALA 1:25

0 1 2 m

PROJETO SEM NOME

Ambiente 1

Medidas em centímetros.

As medidas devem ser conferidas no local.

ESCALA

1:25

FOLHA A3

31/10/2026

AMBIENTE 2

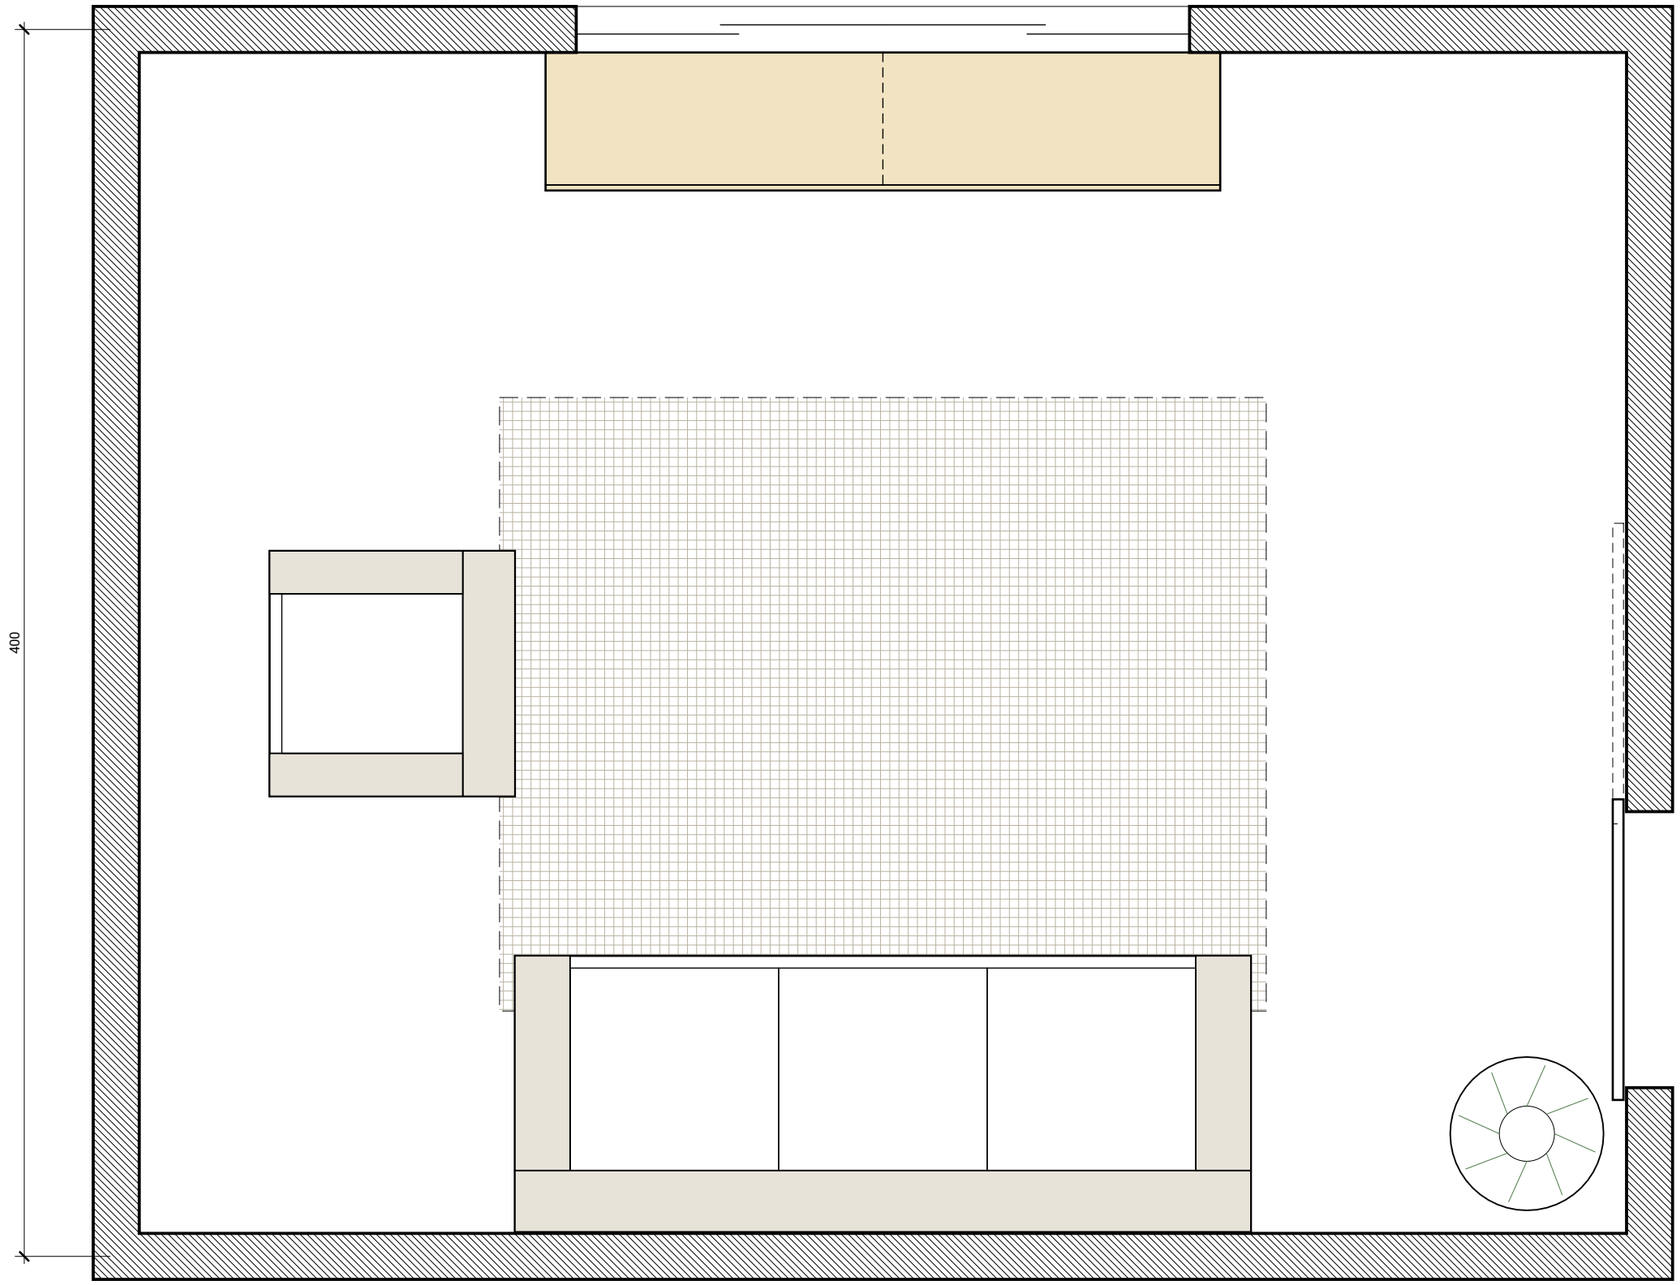

ESCALA 1:20

0 1 m

PROJETO SEM NOME

Ambiente 2

Medidas em centímetros.

As medidas devem ser conferidas no local.

ESCALA

1:20

FOLHA A3

31/10/2026